


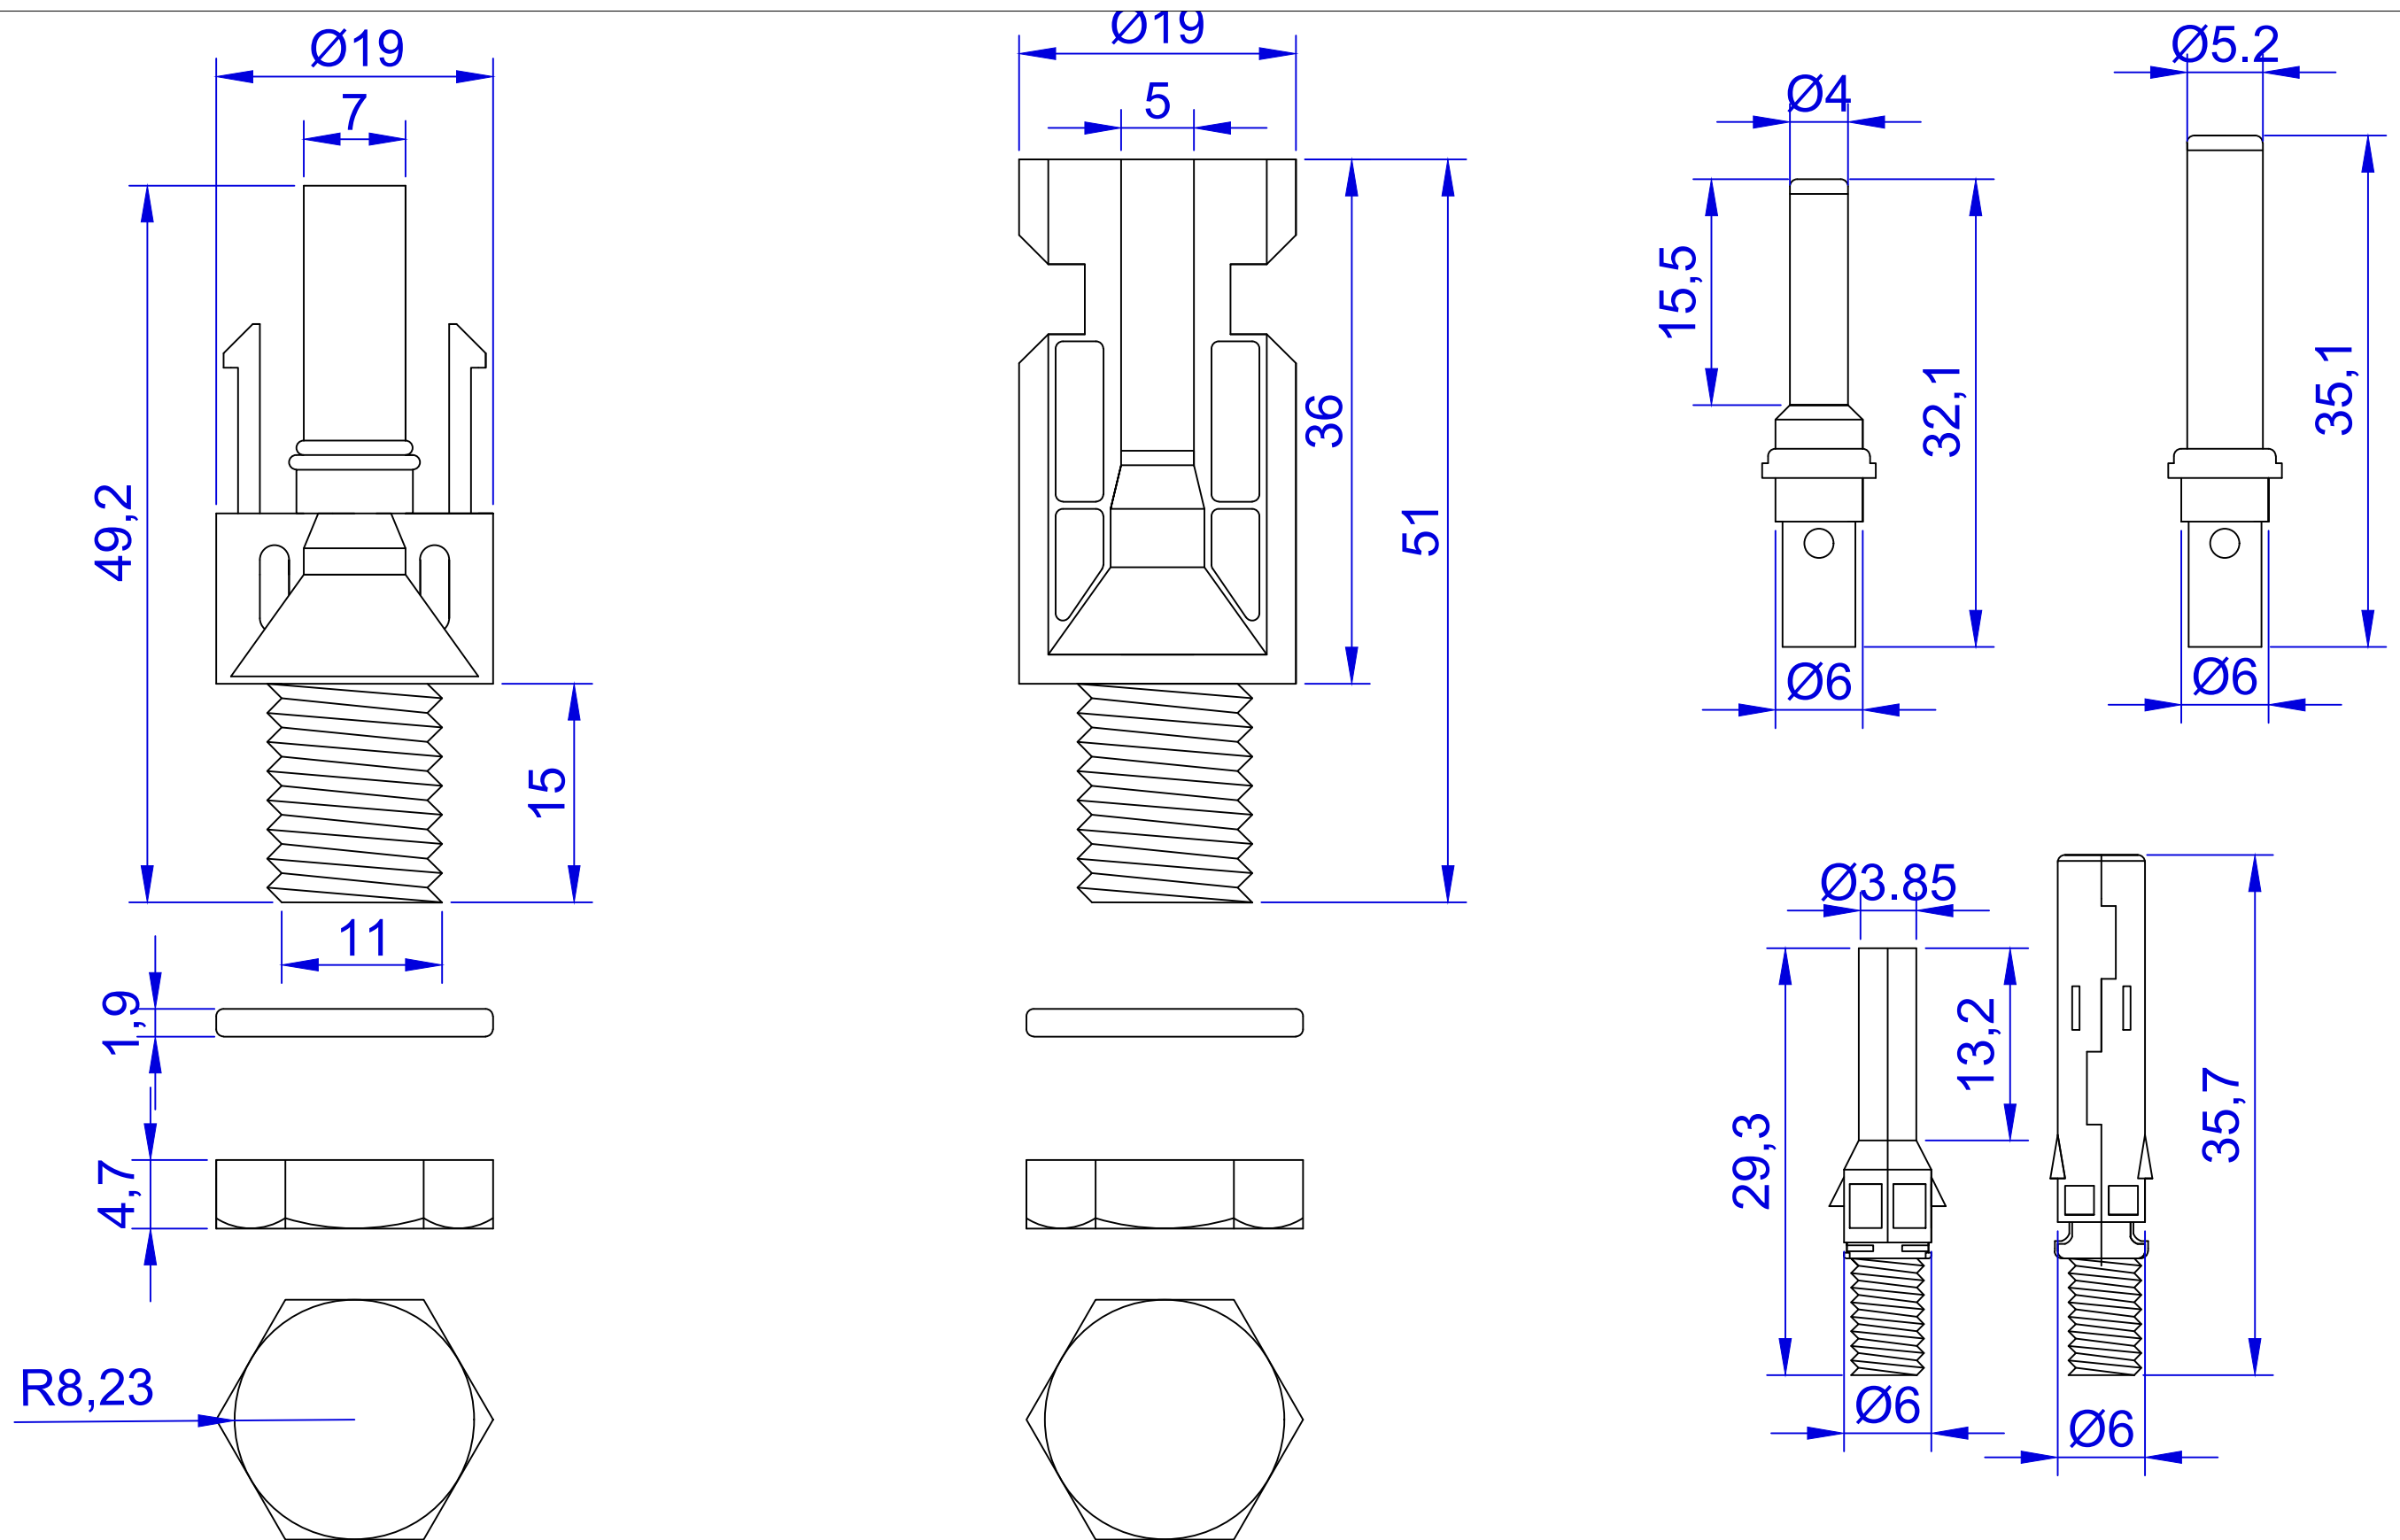

Group Members
 Ammar Asad
 Rabia Zafar
 Zain
 Rumaisa Fatima
 Hamza Raza

Title:
 Solar
 Connectors

Project Name:
 Solar Farm

Units cm

Drawn By:
 Hamza Raza

Front view drawings

Date of Submission:
 16th December

Supervised By:
 Ammar Asad Warraich

Class:
 BEE-17-D

page no of